
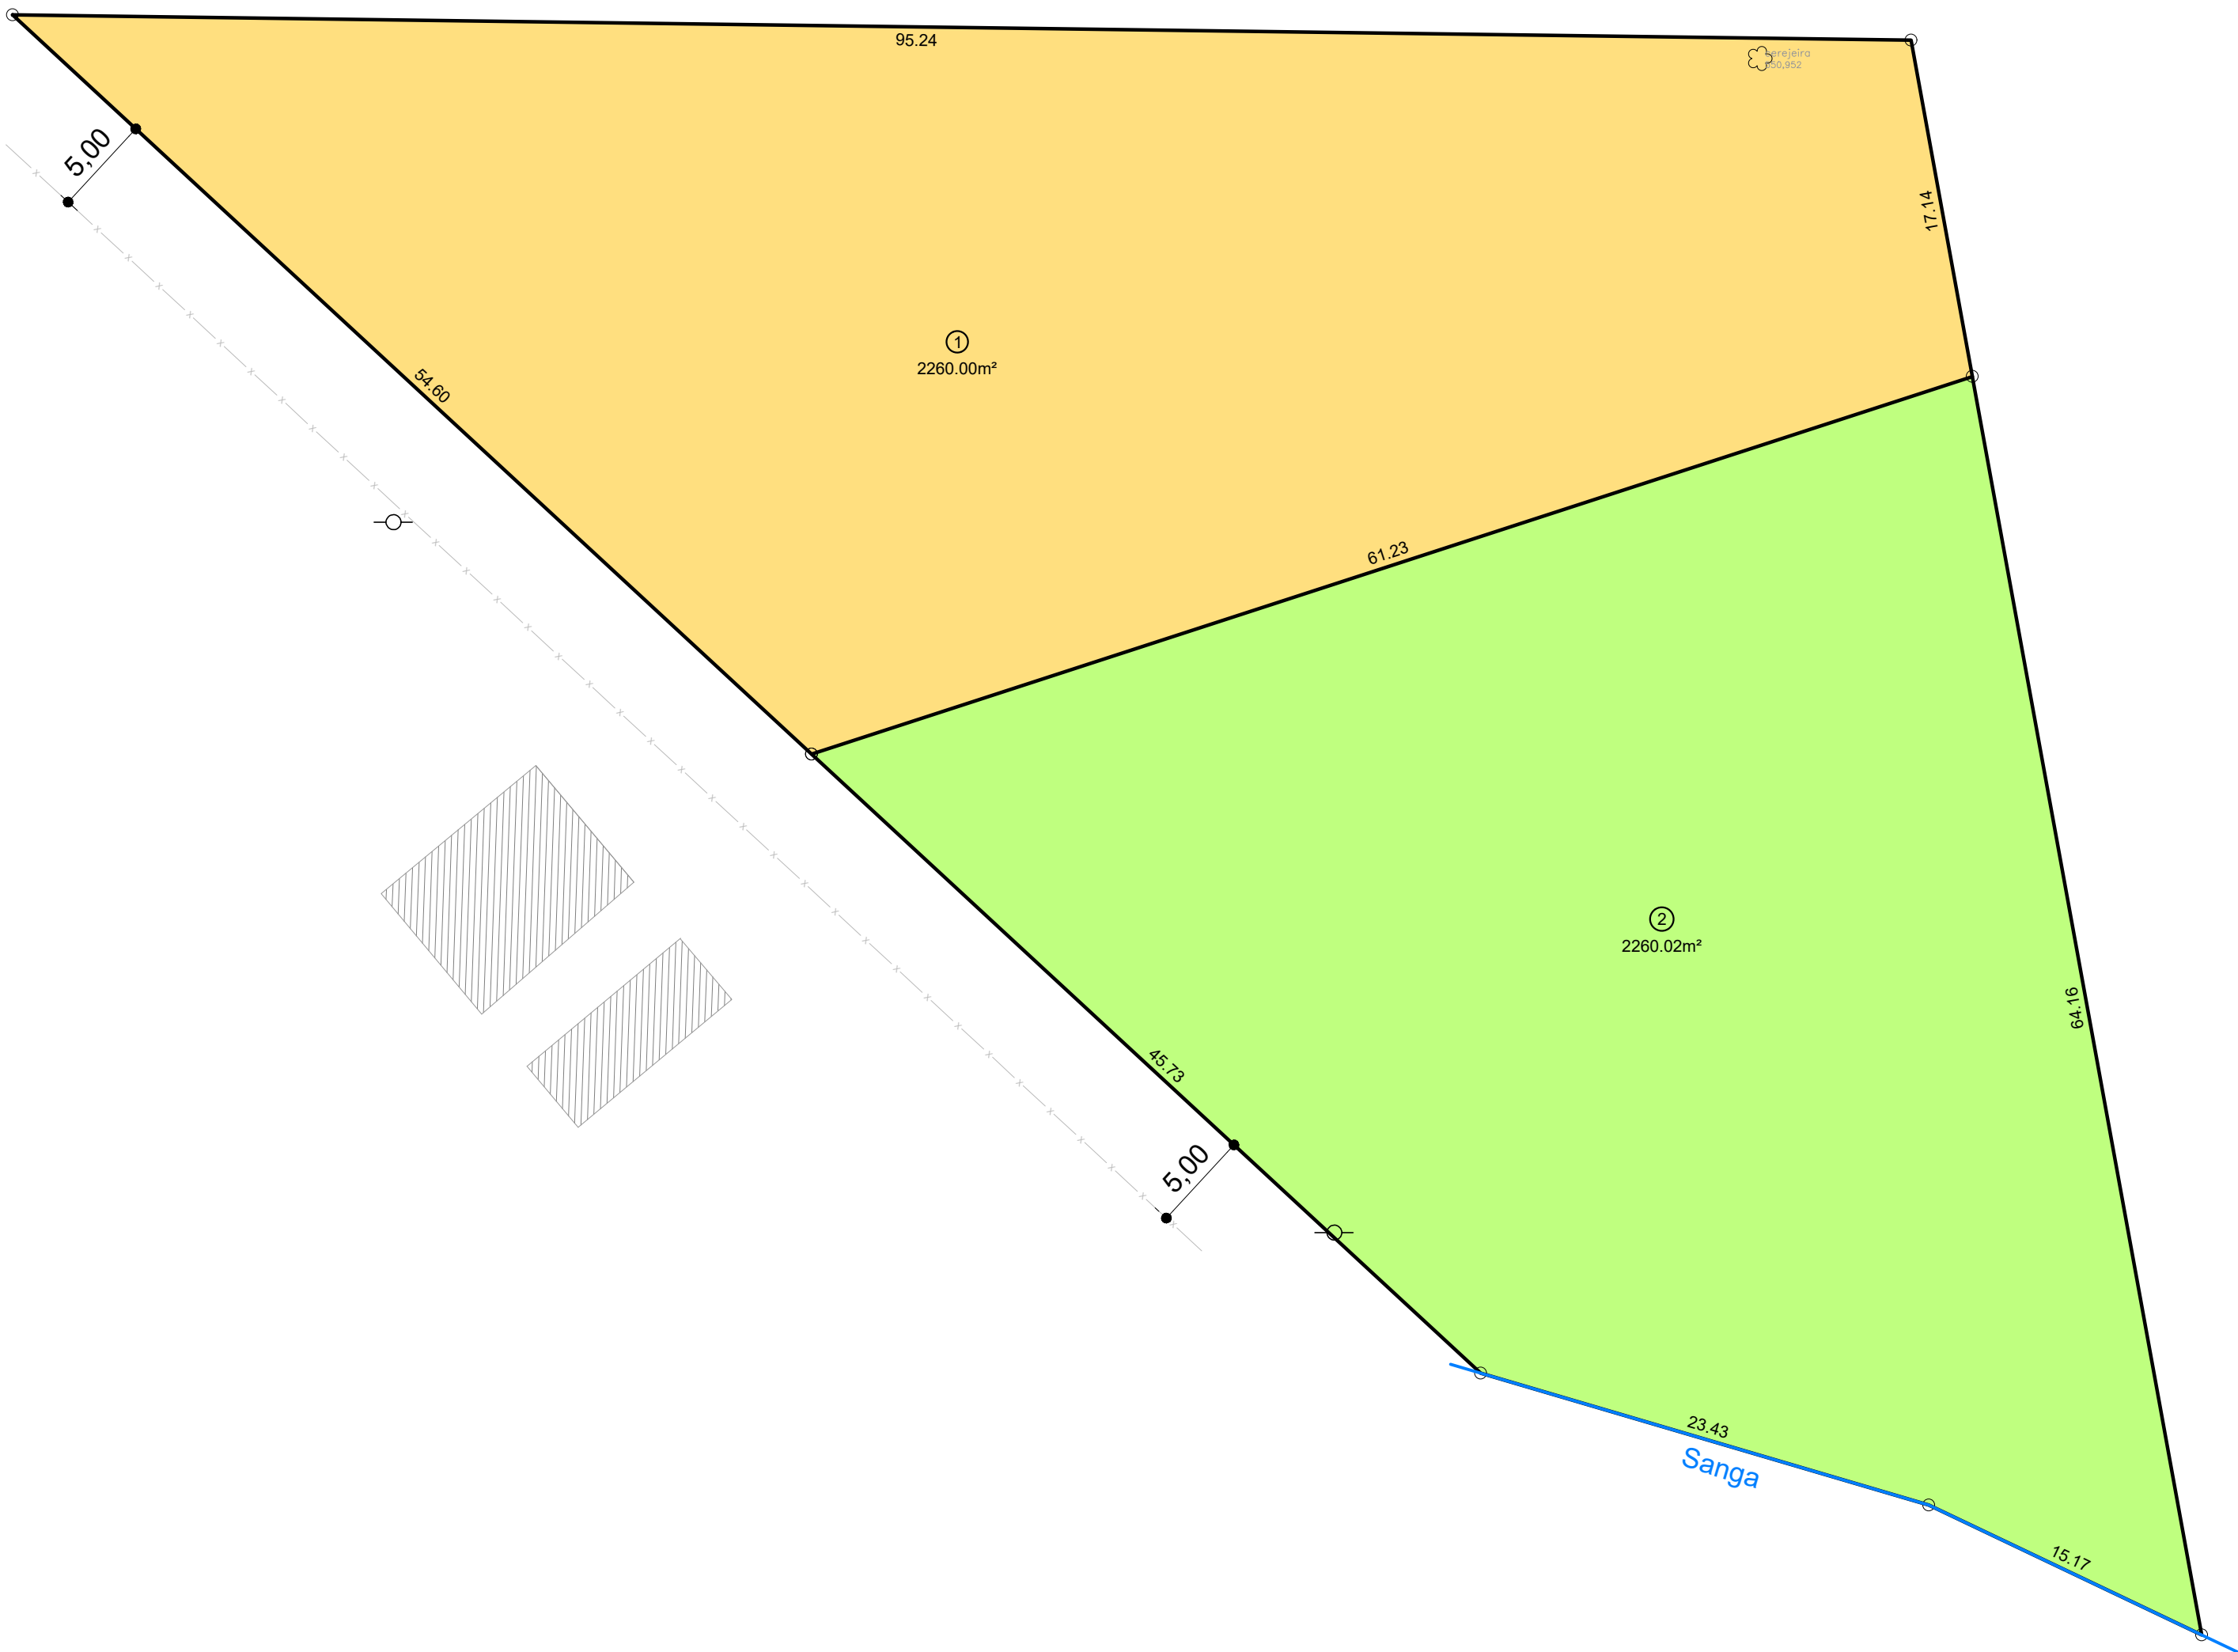


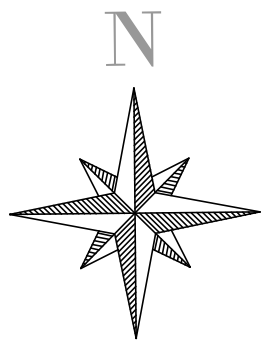

REVISÃO	DESCRIÇÃO	DATA
00	EMIÇÃO	18/12/2020

PROJETO EXECUTIVO DE ENGENHARIA

CONTRATADA	CONTRATANTE
	- CPF: -

SITIOS
Est. Cachoeirão — São José dos Ricci
Divisão de gleba para sitios

AUTORIA DO PROJETO:		CONTRATANTE:	
AUTOR DO PROJETO:		-	
CONSELHO NÚMERO:			
DATA:	ESCALA:	EDITORACÃO GRÁFICA: RAFAEL SOARES	
-	-		
TÍTULO DOS DESENHOS:		PRANCHA:	
		01/01	